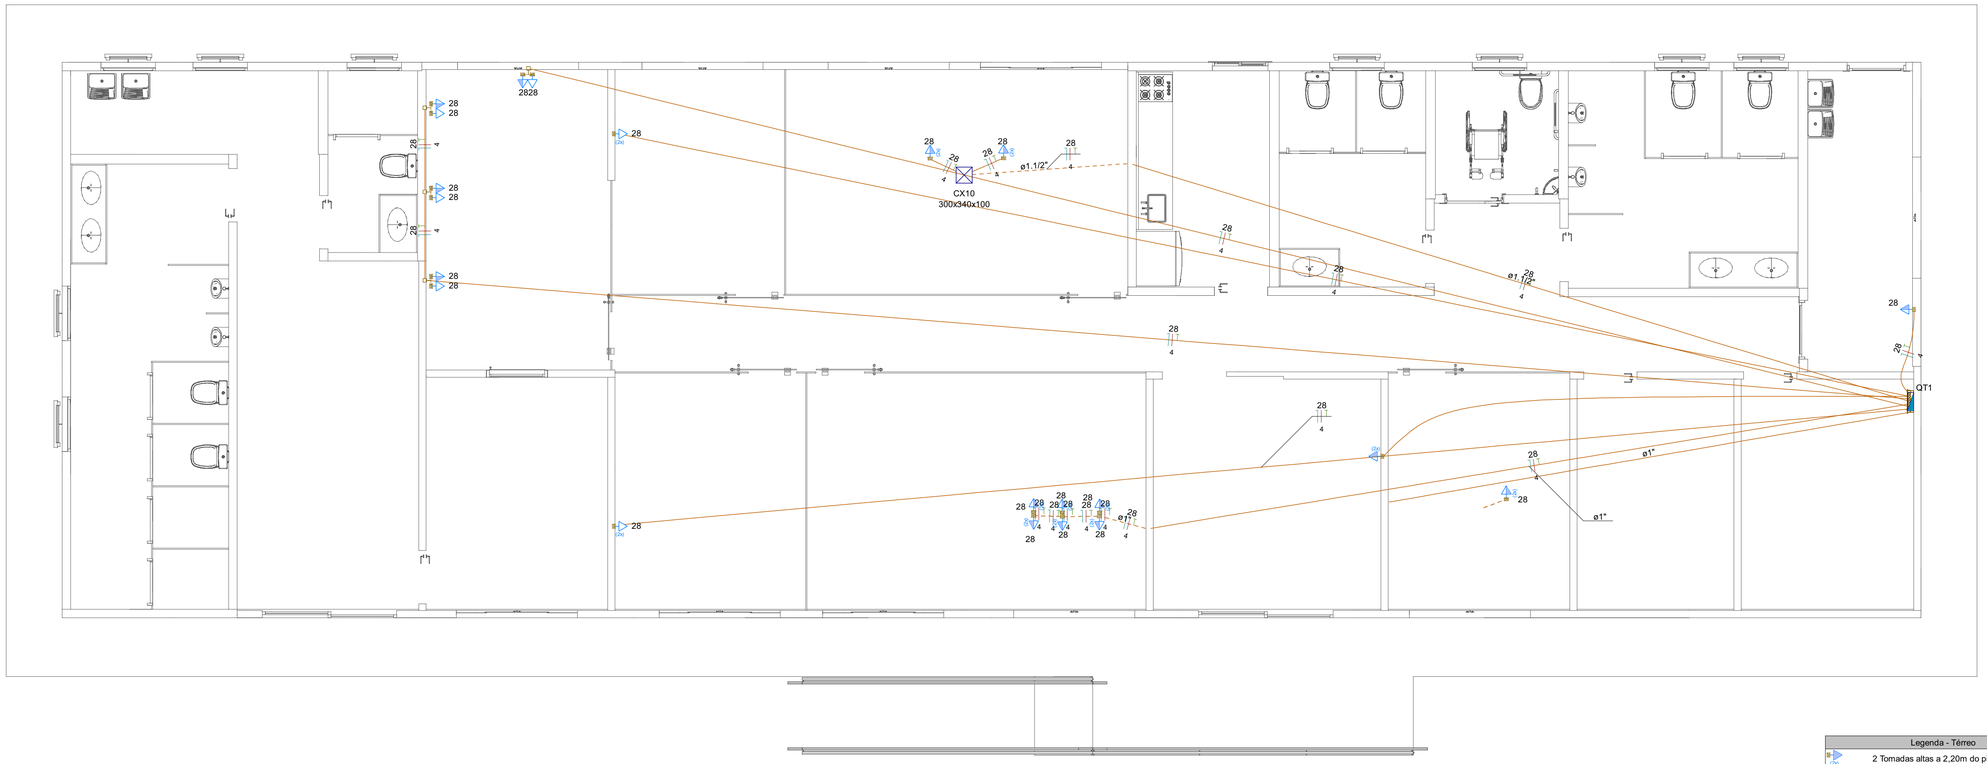


Legenda de condutos - Térreo
Cabeamento
Teto
Média
Piso
Elétrica
Direta
Teto
Alta
Média
Baixa
Piso
Elétrica (Rede Estabilizada)
Direta
Teto
Média
Piso

Lista de materiais - Térreo - Parte 1	
Cabeamento	
Acessórios Cabeamento - Metálico	
Conector RJ45 (CMBv)	21 pç
Acessórios p/ eletrodutos	
Caixa PVC 4x2"	21 pç
Caixa de passagem - embutir	
PVC (ref Krona) 30x20 mm	6 pç
30x34 mm Piso	3 pç
Dispositivo de Cabeamento - embutir	
Placa 2x4" - Bege 1 módulo - RJ45	21 pç
Eletroduto PVC flexível	
Eletroduto leve 1"	5.2 m
3/4"	175.83 m
Eletroduto pesado 1.1/2"	3.4 m
Elétrica	
Acessórios p/ eletrodutos	
Arruela zamak 3"	3 pç
Cabeçote p/ Entrada de Energia 1"	2 pç
Caixa PVC 4x2"	98 pç

Lista de materiais - Térreo - Parte 2	
Curva S 1"	3 pç
Fitas Aço Inox	3 pç
Luva aço galvan. leve 4"	2 pç
Acessórios uso geral	
Arruela de pressão galvan. 1/4"	6 pç
Bucha de nylon S6	8 pç
Parafuso fenda galvan. cab. panela 4,8x45mm autoatarrachante	8 pç
Cabo Unipolar (cobre)	
Isol.PVC - 450/750V 1.5 mm² - Amarelo	155.9 m
1.5 mm² - Azul claro	246.11 m
1.5 mm² - Branco	84.33 m
1.5 mm² - Preto	125.8 m
1.5 mm² - Vermelho	81.08 m
10 mm² - Azul claro	27.52 m
10 mm² - Preto	27.52 m
10 mm² - Verde-amarelo	27.52 m
2.5 mm² - Azul claro	367.27 m
2.5 mm² - Branco	265.33 m
2.5 mm² - Preto	303.58 m
2.5 mm² - Verde-amarelo	288.2 m
2.5 mm² - Vermelho	234.9 m

Lista de materiais - Térreo - Parte 3	
4 mm² - Azul claro	134.51 m
4 mm² - Branco	98.3 m
4 mm² - Verde-amarelo	122.85 m
4 mm² - Vermelho	36.2 m
6 mm² - Branco	59.75 m
6 mm² - Verde-amarelo	59.75 m
6 mm² - Vermelho	59.75 m
Isol.PVC - 450/750V (ref. Pirastic Ecoplus BWF Flexível)	
16 mm² - Azul claro	21 m
16 mm² - Branco	21 m
16 mm² - Preto	21 m
16 mm² - Verde-amarelo	21 m
16 mm² - Vermelho	21 m
25 mm² - Verde-amarelo	20.94 m
50 mm² - Azul claro	20.94 m
50 mm² - Branco	20.94 m
50 mm² - Preto	20.94 m
50 mm² - Vermelho	20.94 m
70 mm² - Azul claro	1.22 m
70 mm² - Branco	1.22 m
70 mm² - Preto	1.22 m
70 mm² - Vermelho	1.22 m
Caixa de passagem - embutir	
Aço pintada (ref Cemar) 530x530x152 mm	8 pç
Dispositivo Elétrico - embutido	
Placa 2x4" Interruptor paralelo - 1 tecla	2 pç

Lista de materiais - Térreo - Parte 4	
Interruptor simples - 1 tecla	18 pç
Placa c/ furo	14 pç
Placa p/ 1 função	20 pç
Placa p/ 2 funções	44 pç
Tomada hexagonal (NBR 14136) 2P+T 10A	11 pç
S/ placa	
Tomada hexagonal (NBR 14136) (2) 2P+T 10A	9 pç
Tomada hexagonal (NBR 14136) (2) 2P+T 20A	35 pç
Tomada hexagonal (NBR 14136) 2P+T 10A	9 pç
Dispositivo de Proteção	
Disjuntor Unipolar Termomagnético - norma DIN (Curva C)	
10 A - 3 kA	11 pç
16 A - 3 kA	2 pç
50 A - 3 kA	1 pç
Disjuntor bipolar termomagnético (380 V/220 V) - DIN (Curva B)	
10 A - 4.5 kA	10 pç
16 A - 4.5 kA	1 pç
25 A - 4.5 kA	2 pç
Disjuntor tetrapolar DR (3fases/neutro - In 30mA) (220/127 V) - DIN (Curva C)	
32 A - 6 kA	1 pç
40 A - 6 kA	2 pç
80 A - 20 kA	1 pç
Disjuntor tetrapolar termomagnético caixa moldada (380/415 V)	
150 A - 18 kA	1 pç
80 A - 30 kA	1 pç
Dispositivo de proteção contra surto	
175 V - 8 kA	8 pç
Interruptor tetrapolar DR (3 fases/neutro - In 30mA) - DIN	

Lista de materiais - Térreo - Parte 5	
80 A	1 pç
Eletroduto PVC flexível	
Eletroduto leve 1"	59.75 m
3/4"	585.88 m
Eletroduto pesado 4"	141.56 m
Iluminação de emergência	
Bloco autônomo - aclaramento Autonomia 3h - 150lm	11 pç
Luminária e acessórios	
Luminária Led Embutir Ledvance Insert 18W	51 pç
Material p/ entrada serviço	
Armação secundária Padrão energisa	1 pç
Caixa inspeção de aterramento caixa de PVC	1 pç
Haste de aterramento aço/cobre D=15mm, comprimento 2,4m	1 pç
Isoladror roldana 76x79mm	4 pç
Poste auxiliar Padrão energisa	1 pç
Tubo aço galv. vara 6,0m 3"	2 pç
Quadro de medição - ENERGISA	
Unidade consumidora individual	

Lista de materiais - Térreo - Parte 6	
Tipo FP (medidor bifásico ou trifásico - Cat. B1 à T4)	1 pç
Quadro distrib. chapa pintada - sobrepor	
Barr. trif., disj. geral, - DIN (Ref. Moratori)	
Cap. 32 disj. unip. - In barr. 150 A	1 pç
Cap. 50 disj. unip. - In barr. 225 A	1 pç
Elétrica (Rede Estabilizada)	
Acessórios p/ eletrodutos	
Caixa PVC 4x2"	22 pç
Cabo Unipolar (cobre)	
Isol.PVC - 450/750V 4 mm² - Azul claro	159.78 m
4 mm² - Verde-amarelo	159.78 m
4 mm² - Vermelho	159.78 m
Caixa de passagem - embutir	
PVC (ref Krona) 30x34 mm Piso	1 pç
Dispositivo Elétrico - embutido	
Placa 2x4" Interruptor simples - 1 tecla	1 pç
Placa p/ 1 função	9 pç
Placa p/ 2 funções	12 pç
S/ placa	
Tomada hexagonal (NBR 14136) (2) 2P+T 10A	10 pç
Tomada hexagonal (NBR 14136) (2) 2P+T 20A	2 pç
Tomada hexagonal (NBR 14136) 2P+T 10A	9 pç
Dispositivo de Proteção	
Disjuntor Unipolar Termomagnético - norma DIN (Curva C)	

Lista de materiais - Térreo - Parte 7	
10 A - 3 kA	1 pç
32 A - 3 kA	1 pç
Eletroduto PVC flexível	
Eletroduto leve 1"	28.2 m
3/4"	141.98 m
Eletroduto pesado 1.1/2"	17.41 m
Quadro c/ transformador	
Quadro c/ transformador Quadro metálico c/ transformador	1 pç
Lógica	
Acessórios p/ eletrodutos	
Caixa PVC 4x2"	1 pç
Dispositivo Lógica - embutir	
Placa 2x4" Tomada redonda RJ45	1 pç

Legenda - Térreo	
2 Tomadas altas a 2,20m do piso	
2 Tomadas baixas a 0,30m do piso	
2 Tomadas médias a 1,20m do piso	
Bloco autônomo ilum. emergência na parede	
Caixa de passagem 300x200 a 0,30 do piso	
Caixa de passagem 300x200 a 1,20 do piso	
Caixa de passagem 300x340x100 a no piso	
Caixa de passagem 800x800x800 no piso	
Entrada de serviço	
Espera para rede lógica a 0,30m do piso	
Interruptor paralelo 1 tecla - 1,20m do piso	
Interruptor simples 1 tecla - 1,20m do piso	
PAINEL DE LED 34W E COR 6.500K - Embutir	
Quadro com transformador	
Quadro de distribuição	
Quadro de medição	
Tomada RJ45 a 1,20m do piso	
Tomada RJ45 a 0,30m do piso	
Tomada RJ45 a 2,20m do piso	
Tomada alta a 2,20m do piso	
Tomada baixa a 0,30m do piso	
Tomada média a 1,20m do piso	

NETO LARA Engenharia e Incorporação

NETO LARA ENGENHARIA E INCORPORAÇÃO
Av. Perimetral Noroeste, 2398 - Sala 02 - Térreo - CENTRO, Sorriso - MT
CEP 78890-090 - Tel (66)99604-7264

Obra
ESCRITÓRIO AMAGGI EM SISTEMA LIGHT STEEL FRAME
Rodovia BR 364, a 26 quilômetros de Ariquemes, Alto Paraíso - RO

Projetista
THALYTA SOUZA REIS
CREA PA nº 1521704139

Proprietário
AMAGGI EXPORTACAO E IMPORTACAO LTDA
CNPJ nº 77.294.254/0122-81

Projeto
INFRA - REDE ESTABILIZADA

Pavimento
Térreo

Conteúdo
PLANTA BAIXA - REDE ESTABILIZADA

Prancha
1

Conjunto	Pran. Tot.
0	1

Data	Escala	Desenho	Conferência
20/09/2026	Indicada	Eng. Thalyta Reis	R00