
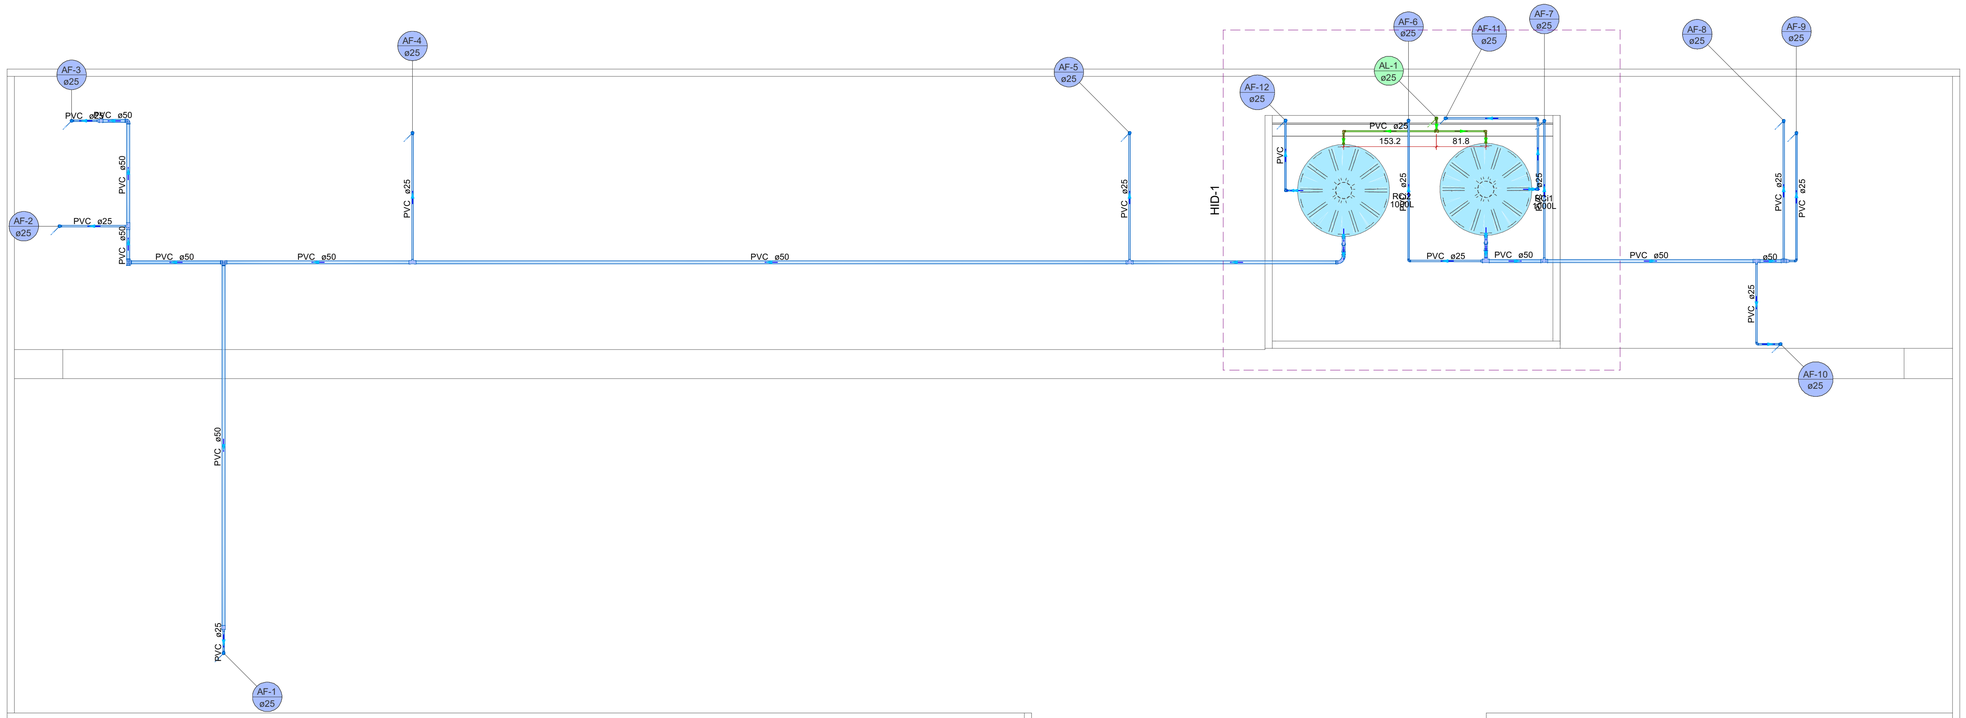


Lista de materiais - Cobertura	
Alimentação	
PVC rígido soldável	
Adapt. sold. c/ registro p/ cx. d'água	
25 mm	2 pç
Joelho 90° soldável	
25 mm	5 pç
Torneira de bóia	
3/4"	2 pç
Tubos	
25 mm	8.06 m
Tê 90 soldável	
25 mm	1 pç
Água fria	
PVC rígido soldável	
Adapt sold c/ flange fixo p cx. d´água	
25 mm - 3/4"	2 pç
Adapt. sold. c/ registro p/ cx. d'água	
25 mm	2 pç
50 mm	2 pç
Bucha de redução sold. longa	
50 mm - 25 mm	4 pç
Curva 90 soldável	
50 mm	5 pç
Joelho 90° soldável	
25 mm	20 pç
50 mm	1 pç
Luva soldável	
50 mm	2 pç
Tubos	
25 mm	33.94 m
50 mm	33.92 m
Tê 90 soldável	
25 mm	2 pç
50 mm	3 pç
Tê de redução 90 soldável	
50 mm - 25 mm	6 pç
Reservatório cilíndrico	
Polietileno	
1000 L	2 pç

Legenda de condutos - Cobertura
Água fria
Alimentação

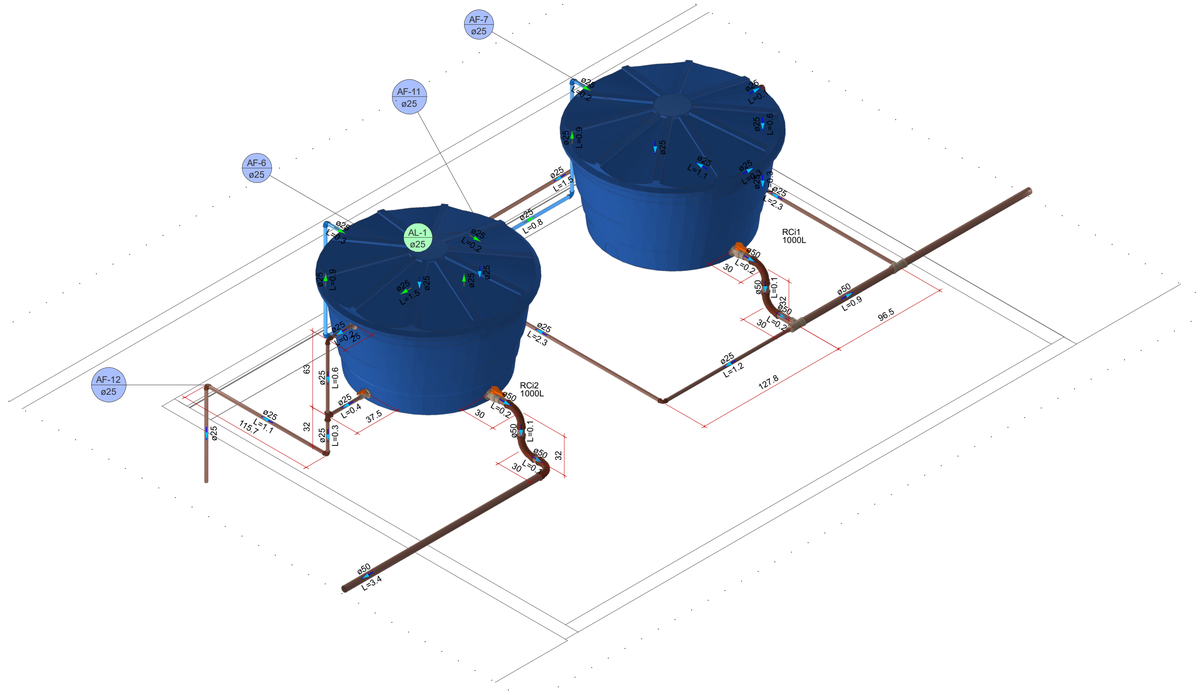

DETALHE HID-1
1:25

NETO LARA ENGENHARIA E INCORPORAÇÃO
Av. Perimetral Noroeste, 2398 - Sala 02 - Térreo - CENTRO, Sorriso - MT
CEP 78890-090 - Tel. (66)99604-7264

Obra
ESCRITÓRIO AMAGGI EM SISTEMA LIGHT STEEL FRAME
Rodovia BR 364, a 26 quilômetros de Ariquemes, Alto Paraíso - RO

Projetista
THALYTA SOUZA REIS
CREA PA nº 1521704139

Proprietário
AMAGGI EXPORTACAO E IMPORTACAO LTDA
CNPJ nº 77.294.254/0122-81

Projeto
HIDRÁULICO

Pavimento
Cobertura

Conteúdo
PLANTA BAIXA - COBERTURA
DETALHAMENTO CAIXA D'ÁGUA
TABELAS E QUADROS

Prancha 4
Conjunto 1 | Pran. Tot. 4

Data	Escala	Desenho	Conferência
16/09/2026	Indicada	Eng. Thalyta Reis	R02