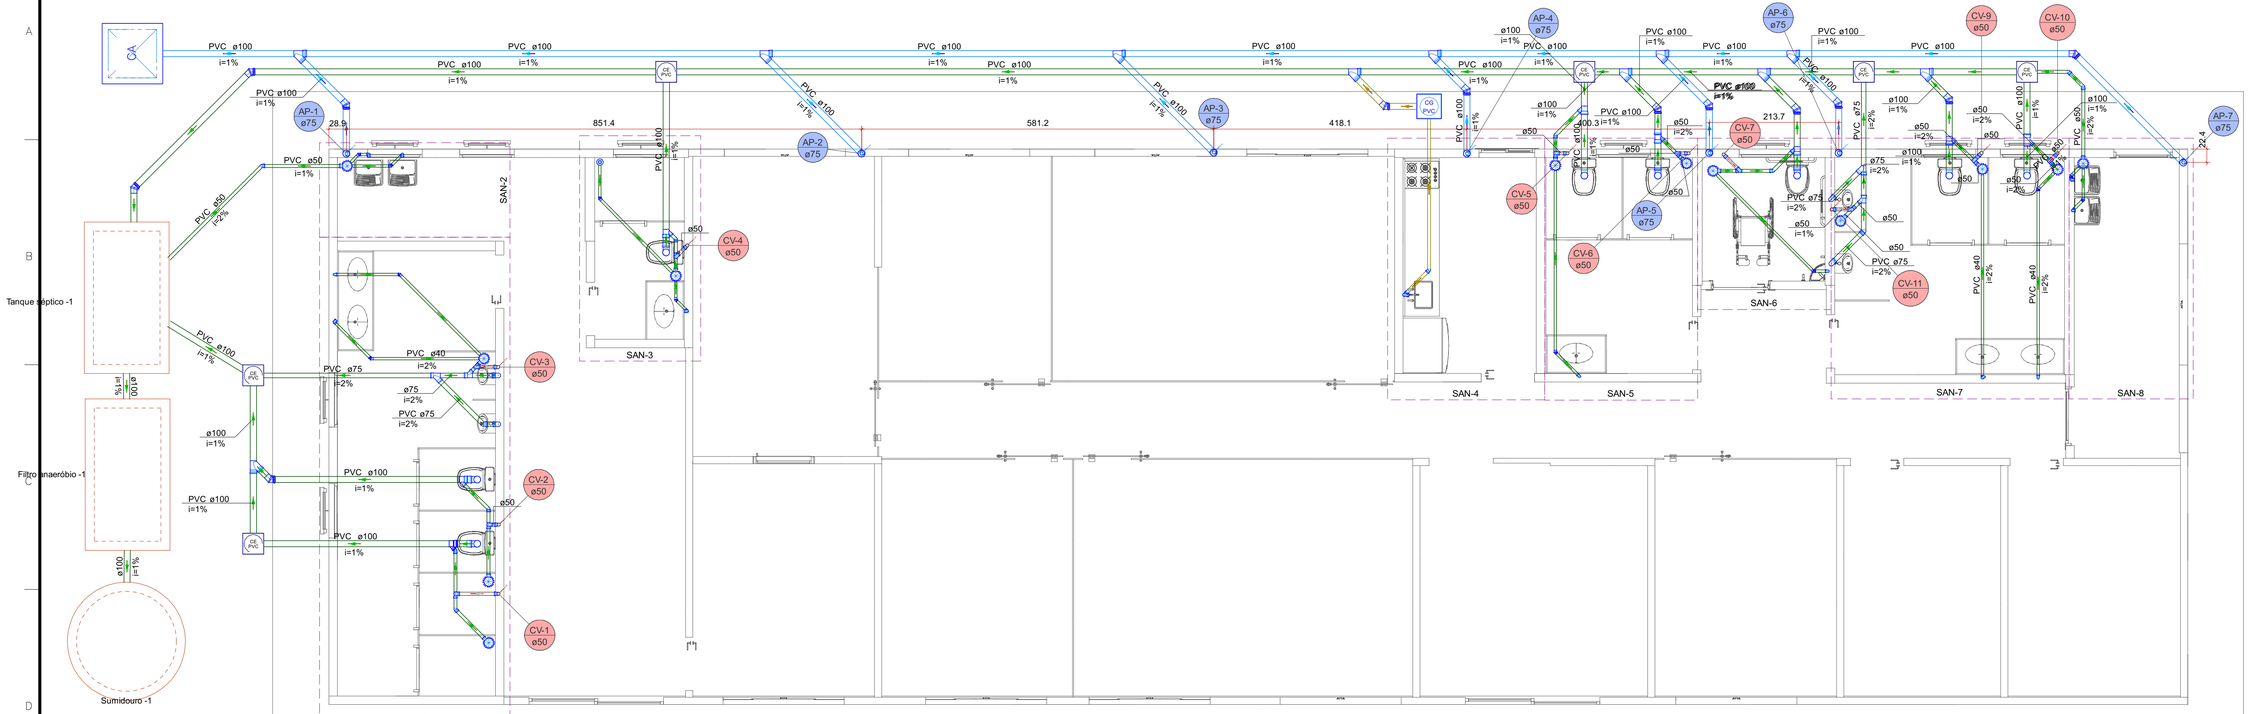


Tanque séptico Tanque séptico -1 (Térreo)

Habitação	Ocupação	Tipo	Número de Ocupantes N	Contribuição de esgoto Unitário (L/pessoa.dia)	Contribuição de esgoto Total (L/dia)	Contribuição de lodo Unitário (L/pessoa.dia)	Contribuição de lodo Total (L/dia)
Escritório	Temporário	Escritório	25	50.00	1250.00	0.20	5.00

Dados:
Intervalo entre limpezas: 2 anos;
Temperatura do mês mais frio: 20 ºC;
K é a taxa de acumulação de lodo digerido: 105 dia;
T é o período de detenção: 1 dia;
N é o número de pessoas ou unidades de contribuição, expressa em unidades (ud);
q é a contribuição de efluente (esgoto), expressa em litros/unidade x dia (L/ud.d);
Lf é a contribuição de lodo fresco, expressa em litros/unidade x dia (L/ud.d);
V é o volume útil, expresso em litros (L).

Volume estimado:
V = 1000 + N * (q * T + K * Lf)
V = 2775.00 L ou 2.77 m³

Dimensões:
Formato: Prismático
Número de câmaras: Câmara única
Comprimento: 220 cm
Largura: 110 cm
Profundidade útil: 120 cm
Volume efetivo: 2.9 m³

Filtro anaeróbio Filtro anaeróbio -1 (Térreo)

Habitação	Ocupação	Tipo	Número de Ocupantes N	Contribuição de esgoto Unitário (L/pessoa.dia)	Contribuição de esgoto Total (L/dia)
Escritório	Temporário	Escritório	25	50.00	1250.00

Dados:
Temperatura do mês mais frio: 20 ºC
T = Tempo de detenção de despejos: 1 dia
C = Contribuição de esgoto: 1250 L/dia

Volume estimado:
V= 1,6 * C * T
V= 1,6 * 1250 * 1
V= 2000 L ou 2 m³

Dimensões:
Formato: Prismático
Comprimento: 165 cm
Largura: 110 cm
Altura do vão livre: 30 cm
Altura total do leito: 120 cm
Volume efetivo: 2.18 m³

Tanque séptico Tanque séptico -1 (Térreo)

Habitação	Ocupação	Tipo	Número de Ocupantes N	Contribuição de esgoto Unitário (L/pessoa.dia)	Contribuição de esgoto Total (L/dia)	Contribuição de lodo Unitário (L/pessoa.dia)	Contribuição de lodo Total (L/dia)
Escritório	Temporário	Escritório	25	50.00	1250.00	0.20	5.00

Dados:
Intervalo entre limpezas: 2 anos;
Temperatura do mês mais frio: 20 ºC;
K é a taxa de acumulação de lodo digerido: 105 dia;
T é o período de detenção: 1 dia;
N é o número de pessoas ou unidades de contribuição, expressa em unidades (ud);
q é a contribuição de efluente (esgoto), expressa em litros/unidade x dia (L/ud.d);
Lf é a contribuição de lodo fresco, expressa em litros/unidade x dia (L/ud.d);
V é o volume útil, expresso em litros (L).

Volume estimado:
V = 1000 + N * (q * T + K * Lf)
V = 2775.00 L ou 2.77 m³

Dimensões:
Formato: Prismático
Número de câmaras: Câmara única
Comprimento: 220 cm
Largura: 110 cm
Profundidade útil: 120 cm
Volume efetivo: 2.9 m³

Legenda de condutos - Térreo
Esgoto
Esgoto (Gordura)
Pluvial
Ventilação

Legenda - Térreo	
	Caixa Sifonada
CA	Caixa de areia pluvial simples
CG PVC	Caixas de Gordura
CX PVC	Caixas de passagem PVC DN 30
	Chuveiro Residencial
	CurVar 45º
	Joelho 45
	Joelho 90- coluna
	Joelho 90- coluna sobe
	Junção invertida
	Junção simples
	Junção simples c/ J45
	Lavatório Residencial com sifão
	Lavatório de Uso Geral
	Mictório de Válvula de Descarga- DN 75mm
	Pia de Cozinha Residencial com Sifão 50mm
	Ramais de Ventilação
	Tanque de Lavar Roupas DN 40mm
	Vaso Sanitário c/ curva 90º

Lista de materiais - Térreo - Parte 1


Esgoto	
Caixas de Passagem	
Caixa de passagem PVC 30 cm	5 pç
PVC Acessórios	
Caixa sifonada 150x150x50	12 pç
Ralo sifonado alt. reg. saída 40	
100 mm - 40 mm	1 pç
Sifão de copo p/ pia e lavatório	
1" - 1.1/2"	7 pç
1" - 2"	1 pç
Sifão flexível c/ Adaptador 1.1/2" - 1.1/2"	4 pç
Sifão flexível p/ Mictório 1.1/4" - 2"	4 pç
Válvula p/ lavatório e tanque 1"	7 pç
Válvula p/ pia 1"	1 pç
Válvula p/ tanque 1 1/2"	4 pç
PVC Esgoto	
Anel de borracha 100mm - 4"	30 pç
50mm - 2"	61 pç
75mm - 3"	16 pç
CurVar 45º 100 mm	6 pç
40 mm	11 pç
Curva 90 curta 100 mm	8 pç
40 mm	12 pç
Joelho 45 50 mm	9 pç
75 mm	2 pç
Joelho 90 100 mm	3 pç
50 mm	10 pç
75 mm	8 pç
Joelho 90 c/anel p/ esgoto secundário 40 mm - 1.1/2"	11 pç
Junção invertida 100 mm x 50 mm	1 pç
75 mm x 50 mm	2 pç

Lista de materiais - Térreo - Parte 2


75 mm x 75 mm	1 pç
Junção simples 100 mm - 50 mm	7 pç
100 mm- 100 mm	4 pç
75 mm 75 mm	1 pç
Luva simples 100 mm	6 pç
75 mm	1 pç
Redução excêntrica 75 mm - 50 mm	4 pç
Tubo rígido c/ ponta lisa 100 mm - 4"	59.8 m
40 mm	30.47 m
50 mm - 2"	13.72 m
75 mm - 3"	11.4 m
Tê sanitário 50 mm - 50 mm	8 pç
Vedação p/ saída de vaso sanitário 100 mm	8 pç
Unidades de tratamento	
Alça Ferro	2 pç
Argamassa Argamassa	0.37 m³
Brita nº3	1.07 m³
nº4	2.18 m³
Concreto Concreto	2 m³
Tampa Hermética	2 pç
Tijolo Furado	187 pç
Esgoto (Gordura)	
Caixas de Passagem	
Caixa de gordura PVC CG 30 cm	1 pç
PVC Esgoto	
Anel de borracha 100mm - 4"	3 pç
50mm - 2"	1 pç
CurVar 45º 100 mm	1 pç
Joelho 45 50 mm	1 pç

Lista de materiais - Térreo - Parte 3


Junção simples 100 mm- 100 mm	1 pç
Luva simples 50 mm	1 pç
Tubo rígido c/ ponta lisa 100 mm - 4"	1.52 m
50 mm - 2"	3.22 m
Pluvial	
Caixas de Passagem	
Caixa de areia pluvial sem grelha CA- 80x80 cm	1 pç
Caixa de passagem PVC 30 cm	1 pç
PVC Esgoto	
Anel de borracha 100mm - 4"	24 pç
75mm - 3"	7 pç
CurVar 45º 100 mm	5 pç
Joelho 90 100 mm	7 pç
Junção simples 100 mm- 100 mm	6 pç
Joelho 90 50 mm	12 pç
Tubo rígido c/ ponta lisa 100 mm - 75 mm	7 pç
Tubo rígido c/ ponta lisa 100 mm - 4"	44.6 m
Ventilação	
PVC Esgoto	
Anel de borracha 50mm - 2"	16 pç
Joelho 90 50 mm	12 pç
Tubo rígido c/ ponta lisa 50 mm - 2"	3.03 m
Tê sanitário 50 mm - 50 mm	2 pç

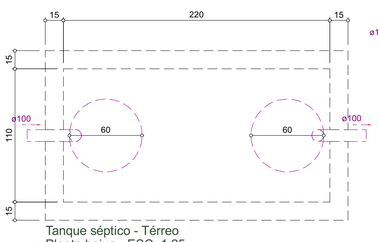


Tanque séptico - Térreo
Planta baixa - ESC. 1:25

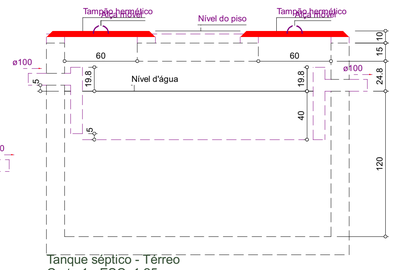


Tanque séptico - Térreo
Corte 1 - ESC. 1:25

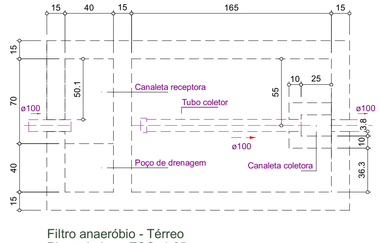

Filtro anaeróbio - Térreo
Planta baixa - ESC. 1:25

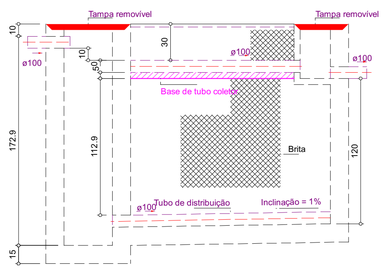

Filtro anaeróbio - Térreo
Corte 1 - ESC. 1:25

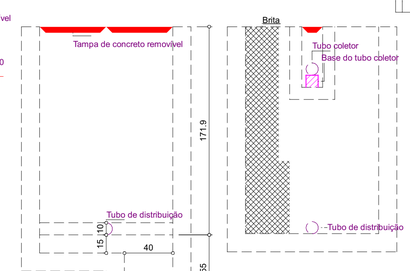

Filtro anaeróbio - Térreo
Corte 2 - ESC. 1:25

NETO LARA ENGENHARIA E INCORPORAÇÃO
Av. Perimetral Noroeste, 2398 - Sala 02 - Térreo - CENTRO, Sorriso - MT
CEP 78890-090 - Tel (66)99604-7264

Obra
ESCRITÓRIO AMAGGI EM SISTEMA LIGHT STEEL FRAME
Rodovia BR 364, a 26 quilômetros de Ariquemes, Alto Paraíso - RO

Projetista
THALYTA SOUZA REIS
CREA PA nº 1521704139

Proprietário
AMAGGI EXPORTACAO E IMPORTACAO LTDA
CNPJ nº 77.294.254/0122-91

Projeto
SANITÁRIO

Pavimento
Térreo

Conteúdo
PLANTA BAIXA - TÉRREO
DETALHAMENTO FOSSA SPÉTICA
DETALHAMENTO FILTRO ANAERÓBIO
TABELAS
QUADROS

Prancha 1
Conjunto 2 | Pran. Tot. 3

Data 24/09/2026 | Escala Indicada | Desenho Eng. Thalyta Reis | Conferência R03