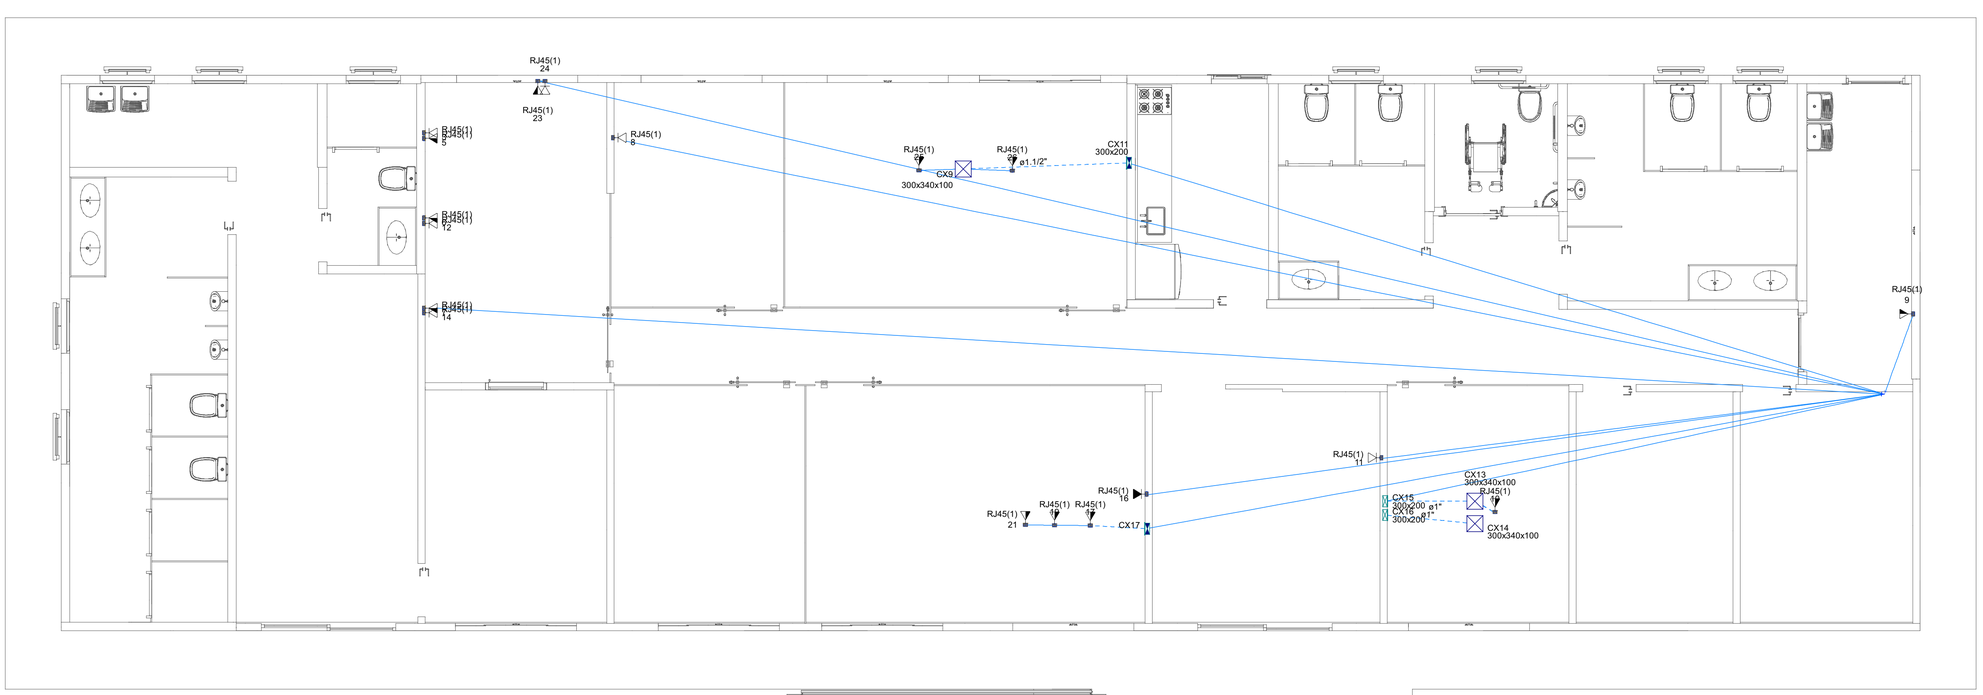


Legenda de condutos - Térreo	
Cabeamento	
	Teto
	Média
	Piso
Elétrica	
	Direta
	Teto
	Alta
	Média
	Baixa
	Piso
Elétrica (Rede Estabilizada)	
	Direta
	Teto
	Média
	Piso

Lista de materiais - Térreo - Parte 1	
Cabeamento	
Acessórios Cabeamento - Metálico	
Conector RJ45 (CMBv)	21 pç
Acessórios p/ eletrodutos	
Caixa PVC 4x2"	21 pç
Caixa de passagem - embutir	
PVC (ref Krona) 30x20 mm	6 pç
30x34 mm Piso	3 pç
Dispositivo de Cabeamento - embutir	
Placa 2x4" - Bege 1 módulo - RJ45	21 pç
Eletroduto PVC flexível	
Eletroduto leve 1"	5.2 m
3/4"	175.83 m
Eletroduto pesado 1.1/2"	3.4 m
Elétrica	
Acessórios p/ eletrodutos	
Arruela zamak 3"	3 pç
Cabeçote p/ Entrada de Energia 1"	2 pç
Caixa PVC 4x2"	98 pç

Lista de materiais - Térreo - Parte 2	
Curva S 1"	3 pç
Fitas	11 pç
Aço Inox	3 pç
Luva aço galvan. leve 4"	2 pç
Acessórios uso geral	
Arruela de pressão galvan. 1/4"	8 pç
Bucha de nylon S6	8 pç
Parafuso fenda galvan. cab. panela 4,8x45mm autoatarrachante	8 pç
Caixa de passagem - embutir	
Aço pintada (ref Cemar) 530x530x152 mm	8 pç
Dispositivo Elétrico - embutido	
Placa 2x4"	8 pç
Interruptor paralelo - 1 tecla	2 pç
Interruptor simples - 1 tecla	18 pç
Placa c/ furo	14 pç
Placa p/ 1 função	20 pç
Placa p/ 2 funções	44 pç
Tomada hexagonal (NBR 14136) 2P+T 10A	11 pç
S/ placa	
Tomada hexagonal (NBR 14136) (2) 2P+T 10A	9 pç
Tomada hexagonal (NBR 14136) (2) 2P+T 20A	35 pç
Tomada hexagonal (NBR 14136) 2P+T 10A	9 pç

Lista de materiais - Térreo - Parte 3	
Dispositivo de Proteção	
Disjuntor Unipolar Termomagnético - norma DIN (Curva C)	
10 A - 3 kA	11 pç
16 A - 3 kA	2 pç
50 A - 3 kA	1 pç
Disjuntor bipolar termomagnético (380 V/220 V) - DIN (Curva B)	
10 A - 4.5 kA	10 pç
16 A - 4.5 kA	1 pç
25 A - 4.5 kA	2 pç
Disjuntor tetrapolar DR (3fases/neutro - In 30mA) (220/127 V) - DIN (Curva C)	
32 A - 6 kA	1 pç
40 A - 6 kA	2 pç
80 A - 20 kA	1 pç
Disjuntor tetrapolar termomagnético caixa moldada (380/415 V)	
150 A - 18 kA	1 pç
80 A - 30 kA	1 pç
Dispositivo de proteção contra surto	
175 V - 8 KA	8 pç
Interruptor tetrapolar DR (3 fases/neutro - In 30mA) - DIN	
80 A	1 pç
Eletroduto PVC flexível	
Eletroduto leve 1"	59.75 m
3/4"	585.88 m
Eletroduto pesado 4"	141.56 m
Iluminação de emergência	
Bloco autônomo - aclaramento	

Lista de materiais - Térreo - Parte 4	
Autonomia 3h - 150lm	11 pç
Luminária e acessórios	
Luminária Led Embutir Ledvance Insert 18W	51 pç
Material p/ entrada serviço	
Armação secundária	
Padrão energisa	1 pç
Caixa inspeção de aterramento caixa de PVC	1 pç
Haste de aterramento aço/cobre D=15mm, comprimento 2,4m	1 pç
Isolador roldana 76x79mm	4 pç
Poste auxiliar	
Padrão energisa	1 pç
Tubo aço galv. vara 6,0m 3"	2 pç
Quadro de medição - ENERGISA	
Unidade consumidora individual	
Tipo FP (medidor bifásico ou trifásico - Cat. B1 à T4)	1 pç
Quadro distrib. chapa pintada - sobrepor	
Barr. Inf., disj. geral, - DIN (Ref. Moratori)	
Cap. 32 disj. unip. - In barr. 150 A	1 pç
Cap. 50 disj. unip. - In barr. 225 A	1 pç
Elétrica (Rede Estabilizada)	
Acessórios p/ eletrodutos	
Caixa PVC 4x2"	22 pç

Lista de materiais - Térreo - Parte 5	
Caixa de passagem - embutir	
PVC (ref Krona) 30x34 mm Piso	1 pç
Dispositivo Elétrico - embutido	
Placa 2x4"	
Interruptor simples - 1 tecla	1 pç
Placa p/ 1 função	9 pç
Placa p/ 2 funções	12 pç
S/ placa	
Tomada hexagonal (NBR 14136) (2) 2P+T 10A	10 pç
Tomada hexagonal (NBR 14136) (2) 2P+T 20A	2 pç
Tomada hexagonal (NBR 14136) 2P+T 10A	9 pç
Dispositivo de Proteção	
Disjuntor Unipolar Termomagnético - norma DIN (Curva C)	
10 A - 3 kA	1 pç
32 A - 3 kA	1 pç
Eletroduto PVC flexível	
Eletroduto leve 1"	28.2 m
3/4"	141.98 m
Eletroduto pesado 1.1/2"	17.41 m
Quadro c/ transformador	
Quadro c/ transformador Quadro metálico c/ transformador	1 pç
Lógica	
Acessórios p/ eletrodutos	
Caixa PVC	

Lista de materiais - Térreo - Parte 6	
4x2"	1 pç
Dispositivo Lógica - embutir	
Placa 2x4 Tomada redonda RJ45	1 pç

Legenda - Térreo	
	2 Tomadas altas a 2,20m do piso
	2 Tomadas baixas a 0,30m do piso
	2 Tomadas médias a 1,20m do piso
	Bloco autônomo ilum. emergência na parede
	Caixa de passagem 300x200 a 0,30 do piso
	Caixa de passagem 300x200 a 1,20 do piso
	Caixa de passagem 300x340x100 a no piso
<>	Caixa de passagem 800x800x800 no piso
	Entrada de serviço
	Espera para rede lógica a 0,30m do piso
	Interruptor paralelo 1 tecla - 1,20m do piso
	Interruptor simples 1 tecla - 1,20m do piso
	PAINEL DE LED 34W E COR 6.500K - Embutir
	Quadro com transformador
<>	Quadro de distribuição
	Quadro de medição
	Tomada RJ45 a 1,20m do piso
	Tomada RJ45 a 0,30m do piso
	Tomada RJ45 a 2,20m do piso
	Tomada alta a 2,20m do piso
	Tomada baixa a 0,30m do piso
	Tomada média a 1,20m do piso

NETO LARA ENGENHARIA E INCORPORAÇÃO
Av. Perimetral Noroeste, 2398 - Sala 02 - Térreo - CENTRO, Sorriso - MT
CEP 78890-090 - Tel (66)99604-7264

Obra
ESCRITÓRIO AMAGGI EM SISTEMA LIGHT STEEL FRAME
Rodovia BR 364, a 26 quilômetros de Ariquemes, Alto Paraíso - RO

Projetista
THALYTA SOUZA REIS
CREA PA nº 1521704139

Proprietário
AMAGGI EXPORTACAO E IMPORTACAO LTDA
CNPJ nº 77.294.254/0122-81

Projeto
INFRA REDE CAT6

Pavimento
Térreo

Conteúdo
Planta Baixa - Cabeamento Rede CAT

Prancha
5

Conjunto 3 | Pran. Tot. 5

Data 20/09/2026 | Escala Indicada | Desenho Eng. Thalyta Reis | Conferência R00