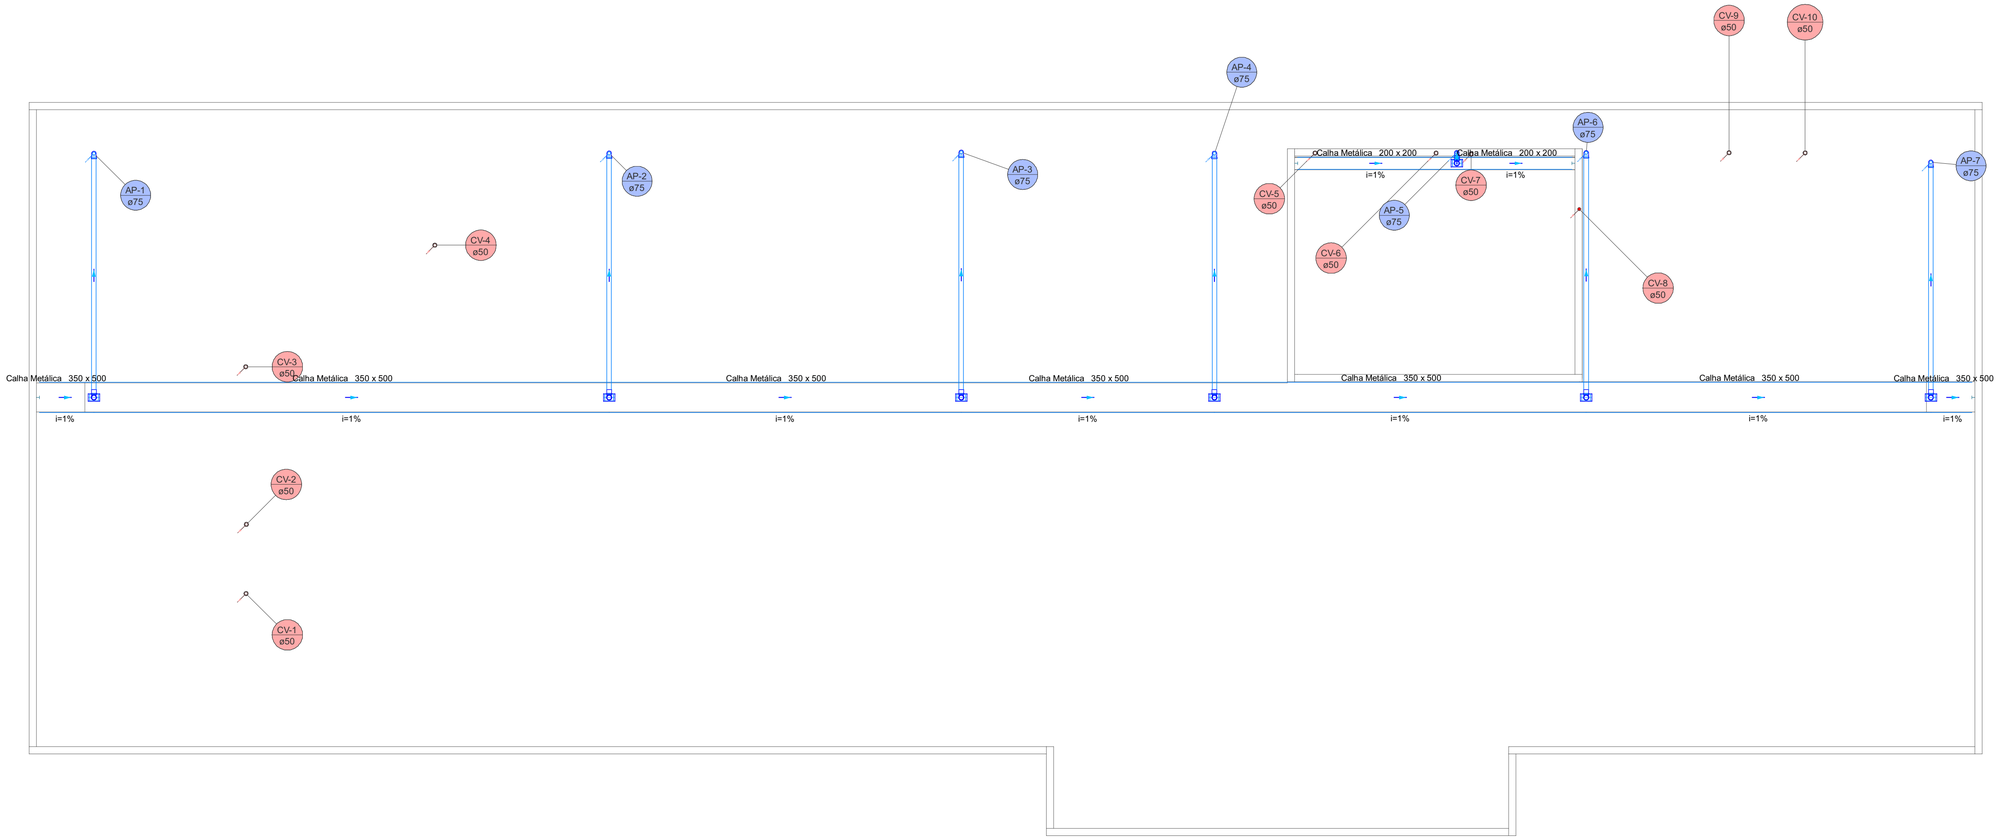


Lista de materiais - Cobertura		
Pluvial		
	Calha metálica	
	Adaptador para bocal semi-circular	
	110 mm x 75 mm	7 pç
	Calha retangular	
	200 mm x 200 mm	4.63 m
	250 mm x 300 mm	32.01 m
	PVC Esgoto	
	Anel de borracha	
	75mm - 3"	14 pç
	Joelho 90	
	75 mm	14 pç
	Tubo PVC ponta-bolsa c/ virola	
	75 mm - 3"	27.57 m
	Tubo rígido c/ ponta lisa	
	75 mm - 3"	25.08 m
Ventilação		
	PVC Esgoto	
	Terminal de ventilação	
	50 mm	9 pç
	Tubo rígido c/ ponta lisa	
	50 mm - 2"	35.23 m

Legenda de condutos - Cobertura
Pluvial
Ventilação

Legenda - Cobertura
Adaptador para bocal semi-circular s/ terminação
Joelho 90- coluna
Joelho 90- desce
Terminal de ventilação- coluna

NETO LARA ENGENHARIA E INCORPORAÇÃO
Av. Perimetral Noroeste, 2398 - Sala 02 - Térreo - CENTRO, Sorriso - MT
CEP 78890-090 - Tel (66)99604-7264

Obra
ESCRITÓRIO AMAGGI EM SISTEMA LIGHT STEEL FRAME
Rodovia BR 364, a 26 quilômetros de Ariquemes, Alto Paraíso - RO

Projetista
THALYTA SOUZA REIS
CREA PA nº 1521704139

Proprietário
AMAGGI EXPORTACAO E IMPORTACAO LTDA
CNPJ nº 77.294.254/0122-81

Projeto
PLUVIAL E SANITÁRIO

Pavimento
Cobertura

Conteúdo
PLANTA BAIXA COBERTURA
PONTOS DE VENTILAÇÃO - SANITÁRIO
TABELAS
QUADROS

Prancha 1

Conjunto	Pran. Tot.
0	1

Data	Escala	Desenho	Conferência
16/09/2026	Indicada	Eng. Thalyta Reis	R02