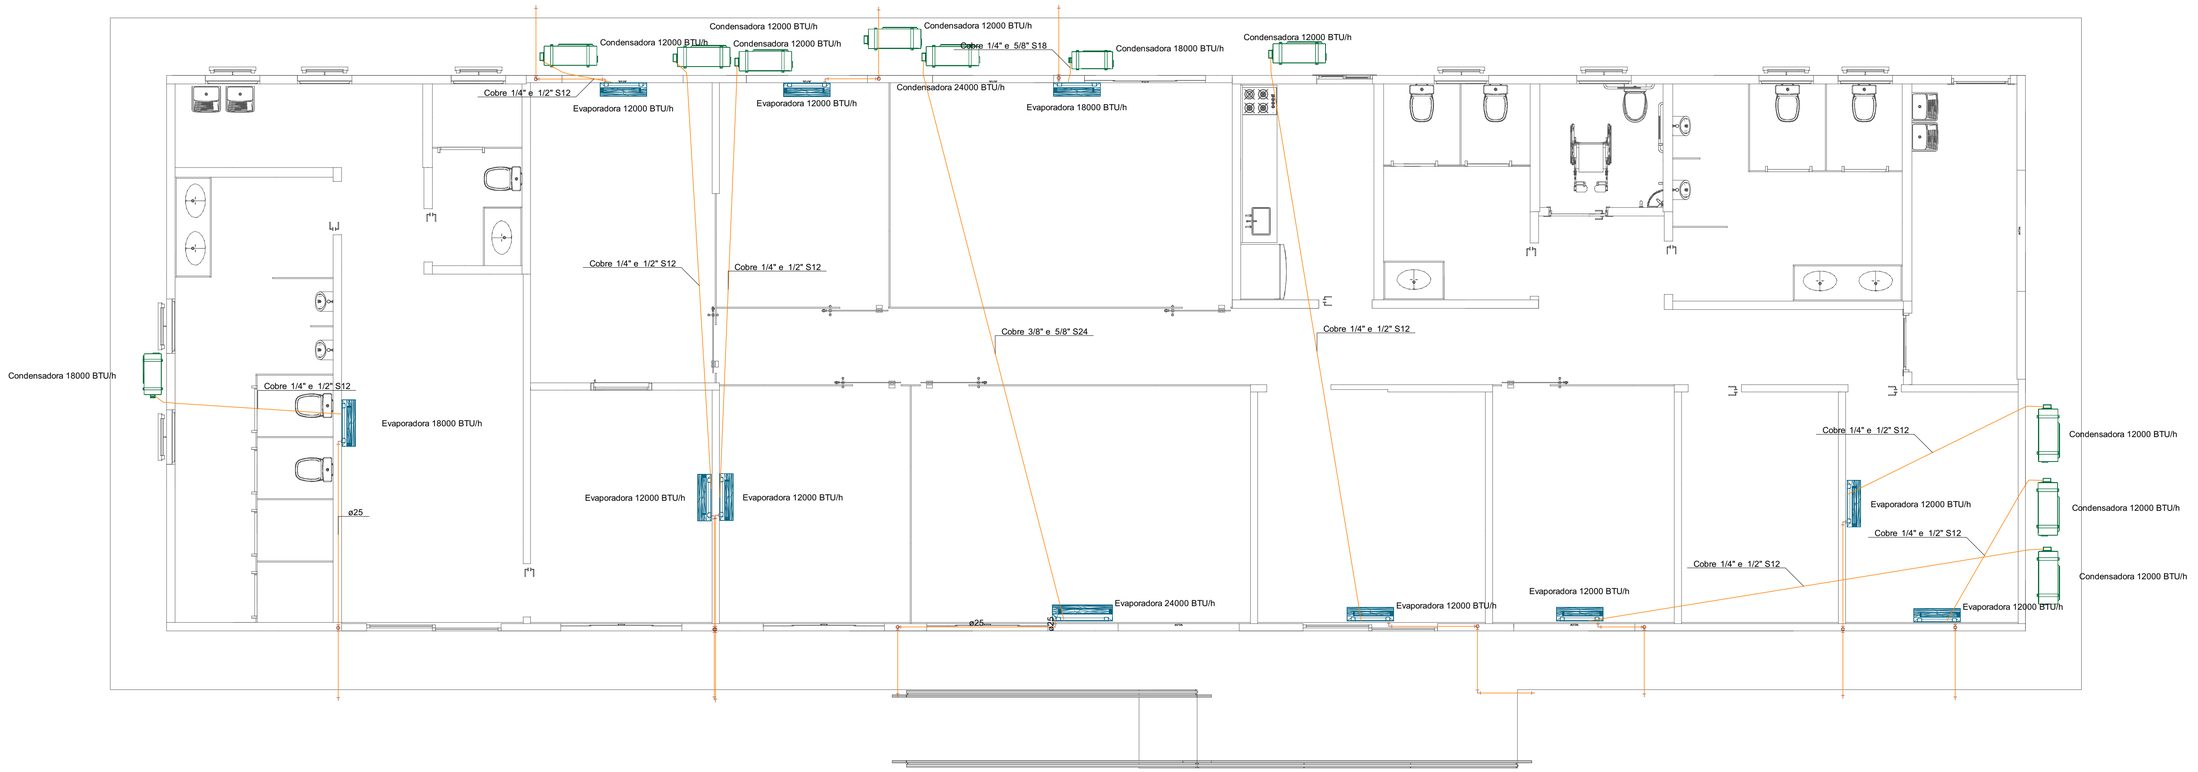


Legenda de condutos - Térreo
Climatização

Lista de materiais - Térreo		
Climatização		
Equipamentos Ar condicionado		
Condensadora Split		
12000 BTU/h	8 pç	
18000 BTU/h	2 pç	
24000 BTU/h	1 pç	
Evaporadora Split		
12000 BTU/h	8 pç	
18000 BTU/h	2 pç	
24000 BTU/h	1 pç	
PVC rígido soldável		
Cap soldável		
25 mm	11 pç	
50 mm	16 pç	
60 mm	4 pç	
Joelho 90º soldável		
25 mm	32 pç	
Tubos		
25 mm	55.22 m	
Segmento de duto		
Cabo PP Tetrapolar Isol.PVC - 0,6/1KV		
#2.5 mm²	71.35 m	
Tubo Isolante Esponjoso		
1/2"	57.53 m	
1/4"	59.89 m	
3/8"	11.46 m	
5/8"	13.82 m	
Tubo de cobre flexível		
1/2"	57.53 m	
1/4"	59.89 m	
3/8"	11.46 m	
5/8"	13.82 m	

NETO LARA
Engenharia e Incorporação

NETO LARA ENGENHARIA E INCORPORAÇÃO
Av. Perimetral Noroeste, 2398 - Sala 02 - Térreo - CENTRO, Sorriso - MT
CEP 78890-090 - Tel (66)99604-7264

Obra
ESCRITÓRIO AMAGGI EM SISTEMA LIGHT STEEL FRAME
Rodovia BR 364, a 26 quilômetros de Ariquemes, Alto Paraíso - RO

Projetista
THALYTA SOUZA REIS
CREA PA nº 1521704139

Proprietário
AMAGGI EXPORTACAO E IMPORTACAO LTDA
CNPJ nº 77.294.254/0122-81

Projeto
CLIMATIZAÇÃO

Pavimento
Térreo

Conteúdo
PLANTA BAIXA -TÉRREO
LISTA DE MATERIAIS
QUADRO

Prancha
1

Conjunto 4 | Pran. Tot. 1

Data	Escala	Desenho	Conferência
16/09/2026	Indicada	Eng. Thalyta Reis	R01