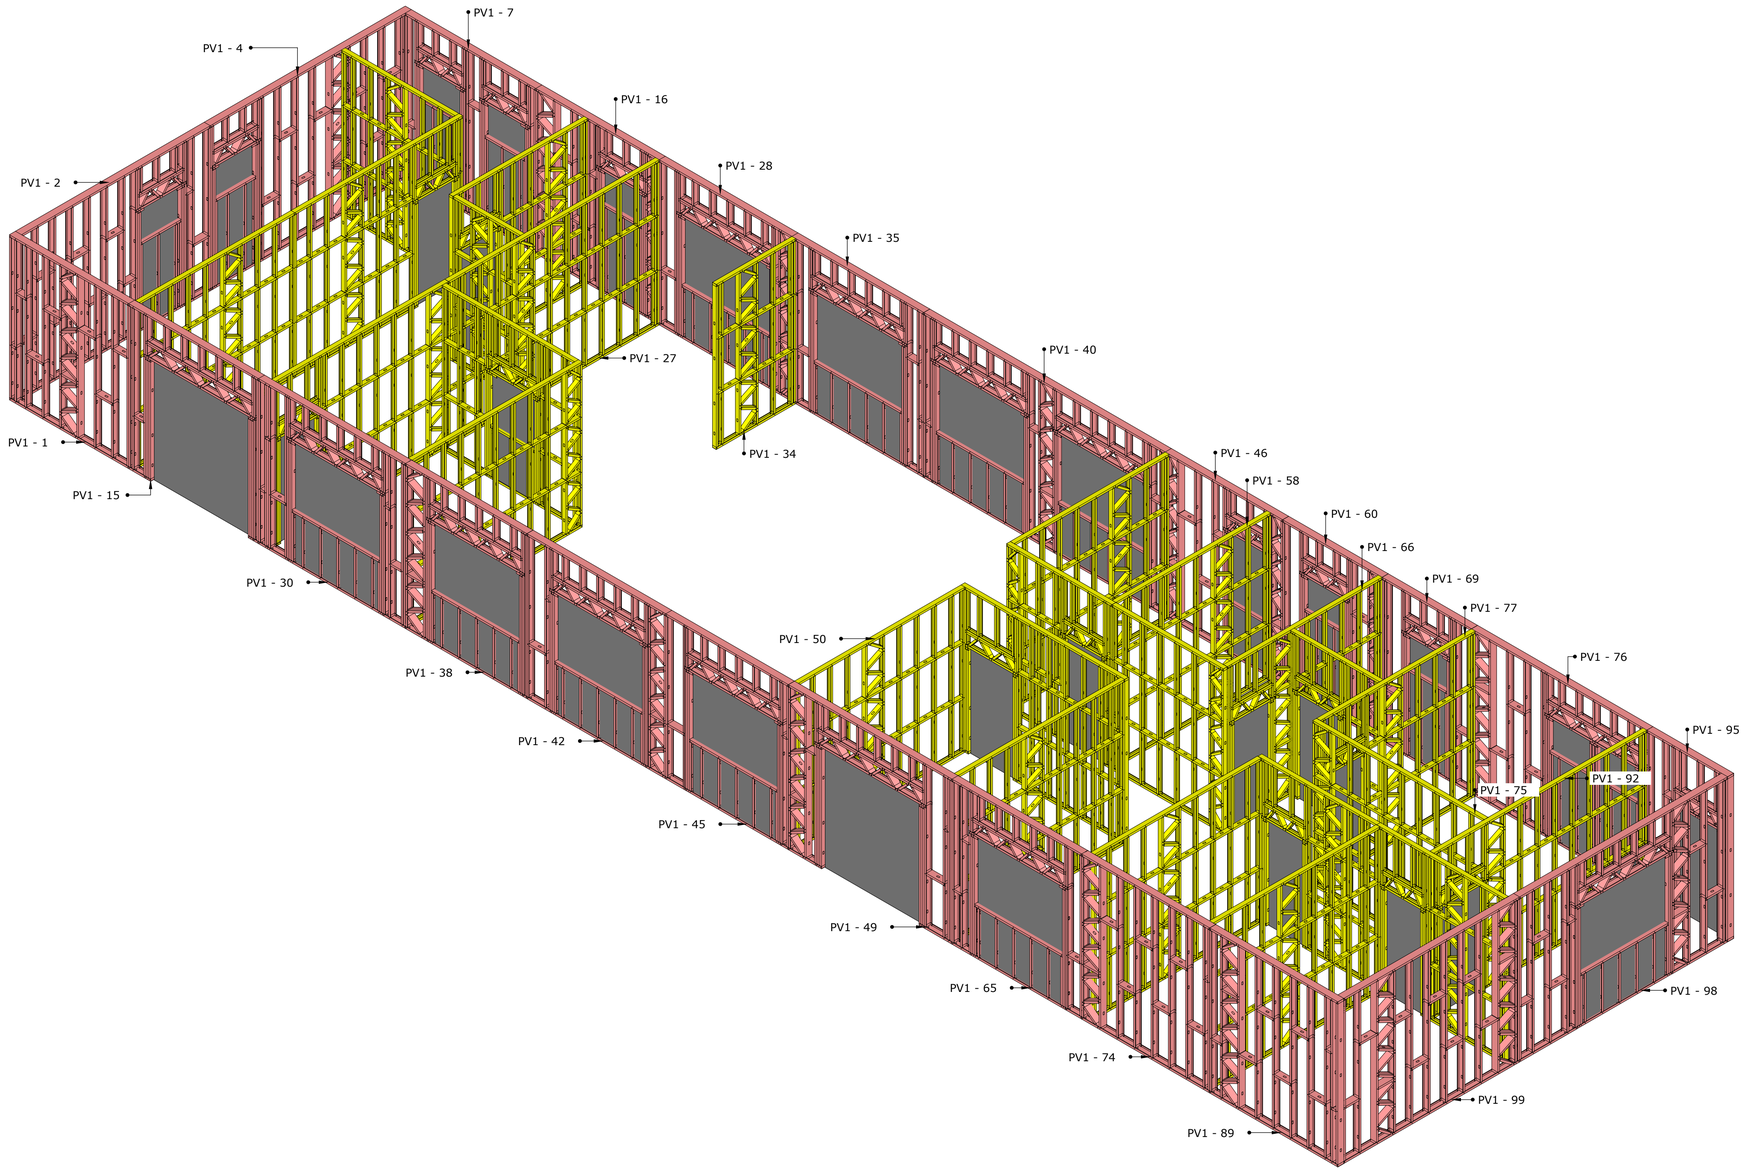


As informações contidas neste desenho são exclusividades da Up rise Framing.
não podem ser copiados, reproduzidos sem autorização prévia.

Entidade do projeto

Data	REV.	Descrição	Responsável

Projeto Estrutural Light Steel Framing

AMAGGI

Informações do Projeto:
AMAGGI EXPORTAÇÃO E IMPORTAÇÃO LTDA.
RODOVIA BR 364, LOTE 06-A-1 KM 543.7,
GLEBA 25 ALTO PARAÍSO - RO

Descrição da Folha:
Isométrica de painéis - PV1

Responsabilidade Técnica::
Engº Roberto Hiroyuki Nakamura
CREA PR-90790/D
ART.:

www.upriseframing.com.br
(42) 98813 - 7718

Up Rise

Link temporário para acesso do formulário DIGITAL

Escala indicada

Revisão: R0

Prancha 01

mm

Detalhamento de Montagem

IMPRIMIR COLORIDO E EM FOLHA A1