

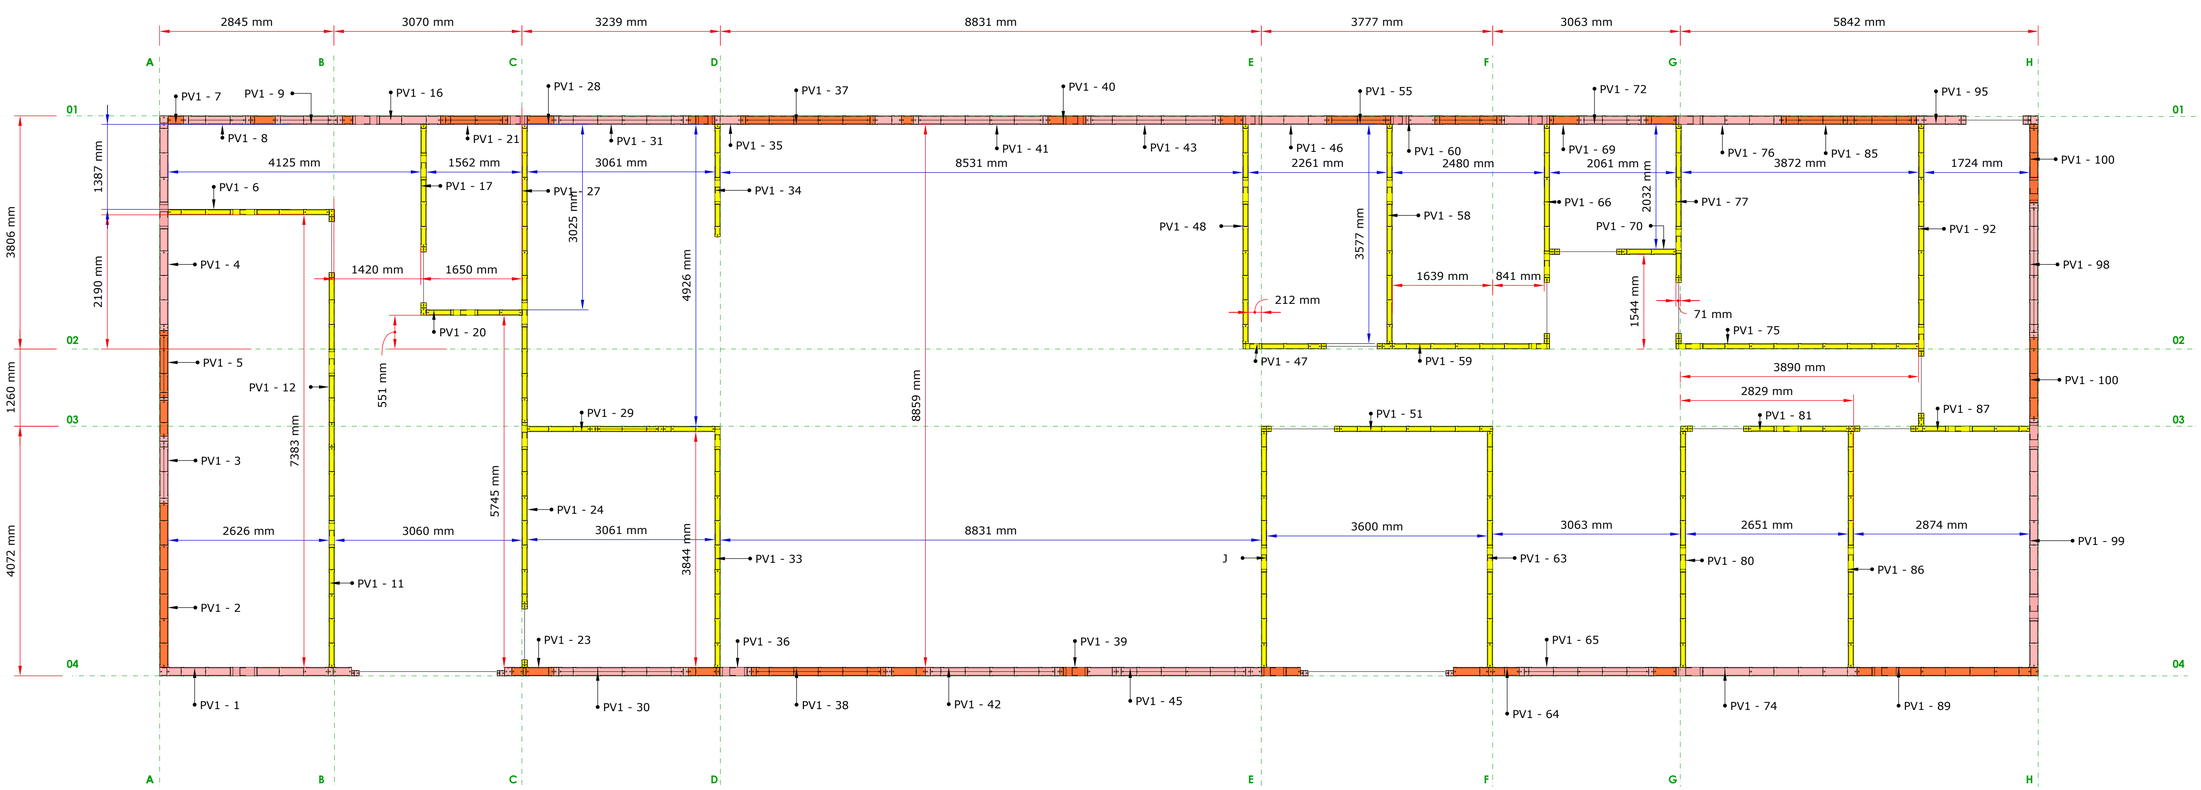



Eixo 01 - escala 1:50

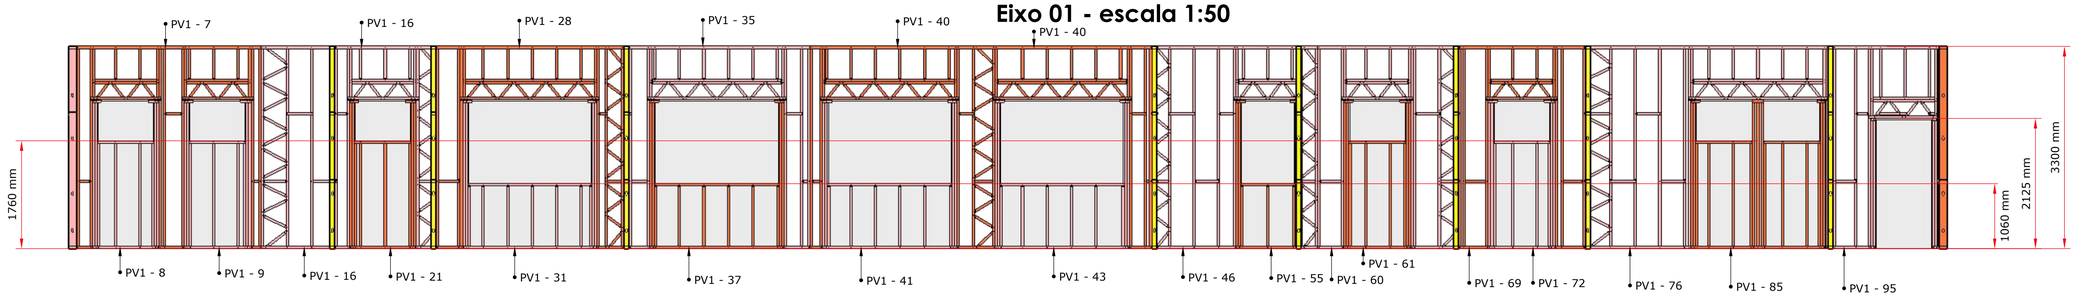


Eixo 02 - escala 1:50

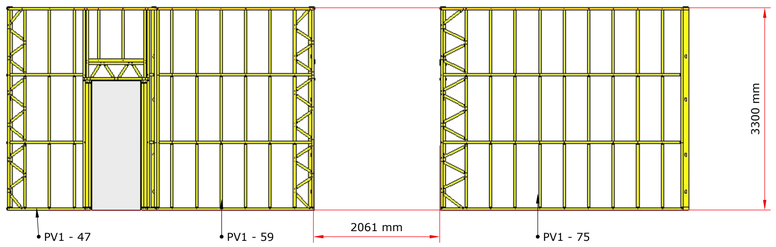

Eixo 03 - escala 1:50

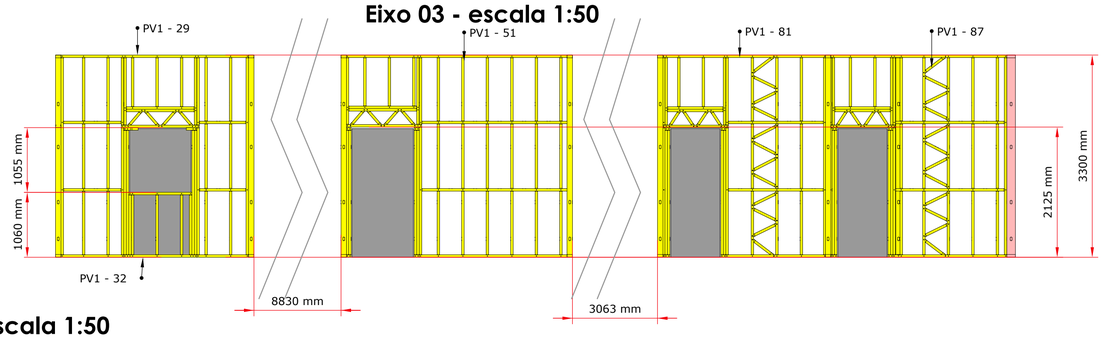

Eixo 04 - escala 1:50

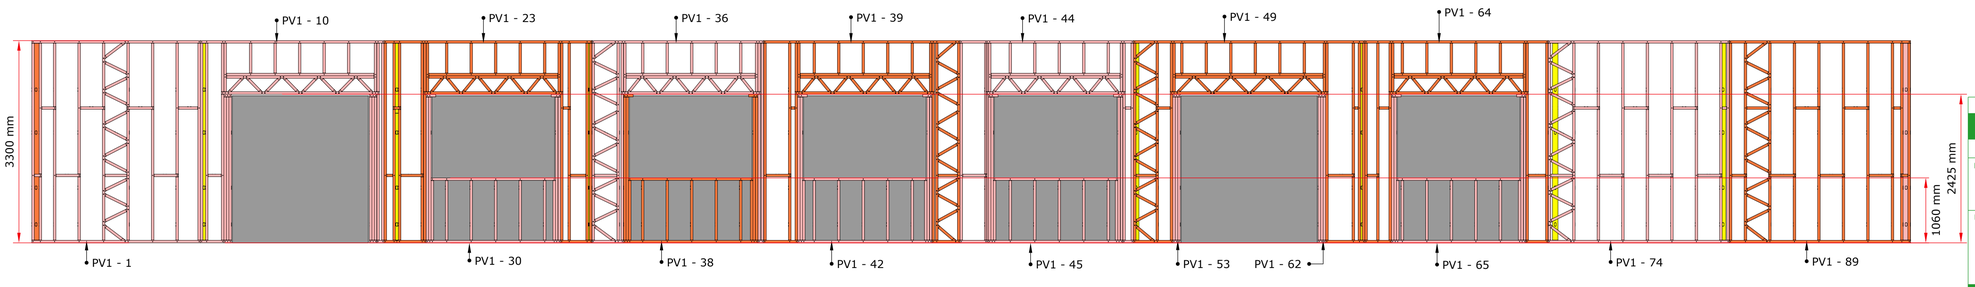

As informações contidas neste desenho são exclusividades da Up rise Framing, não podem ser copiados, reproduzidos sem autorização prévia.

Data	REV.	Descrição	Responsável

Projeto Estrutural Light Steel Framing

AMAGGI

Informações do Projeto:
AMAGGI EXPORTAÇÃO E IMPORTAÇÃO LTDA.
RODOVIA BR 364, LOTE 06-A-1 KM 543,7,
GLEBA 25 ALTO PARAÍSO - RO

Descrição da Folha:
Locação e corte de painéis - PV1

Responsabilidade Técnica::
Engº Roberto Hiroyuki Nakamura
CREA PR-90790/D
ART.:
www.upriseframing.com.br
(42) 98813 - 7718

Up Rise

Link temporário para acesso do formulário DIGITAL

Escala indicada
Revisão: R0
Prancha 02
mm

Detalhamento de Montagem

IMPRIMIR COLORIDO E EM FOLHA A1

Embalagem do projeto