


Eixo A - escala 1:50

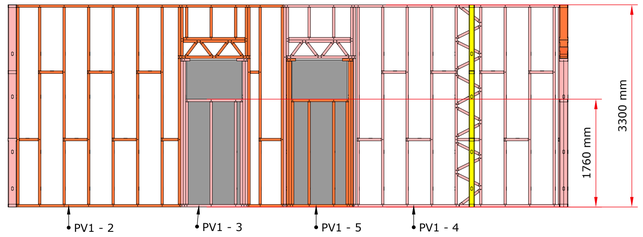


Eixo B - escala 1:50

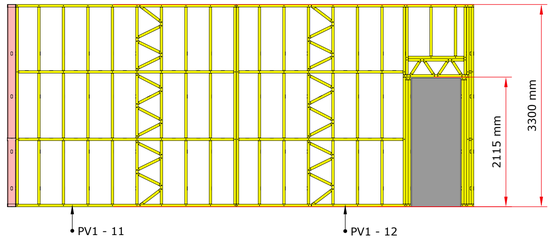


Eixo C - escala 1:50

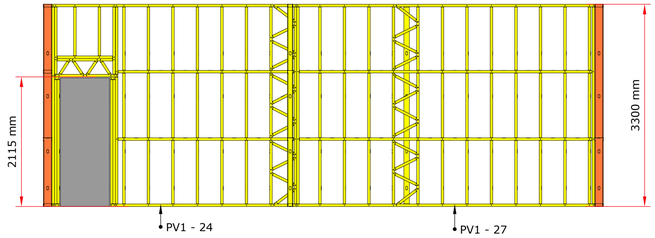


Eixo D - escala 1:50

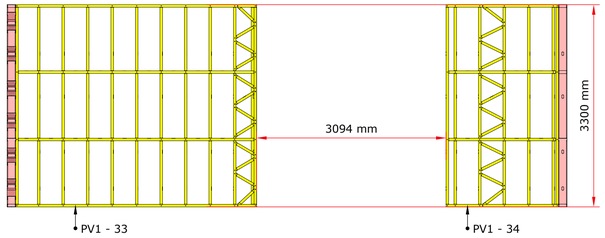


Eixo E - escala 1:50

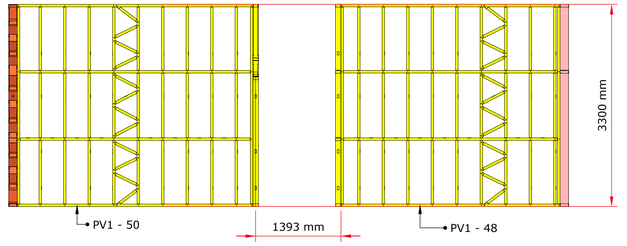


Eixo F - escala 1:50

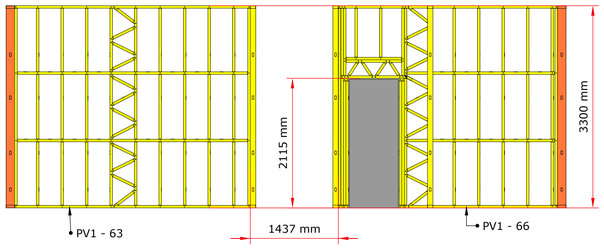


Eixo G - escala 1:50

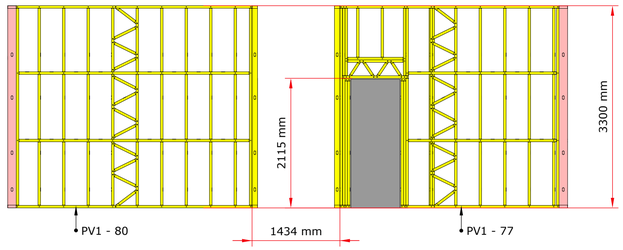

Eixo H - escala 1:50

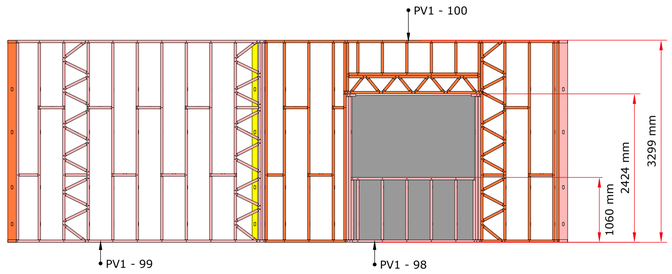

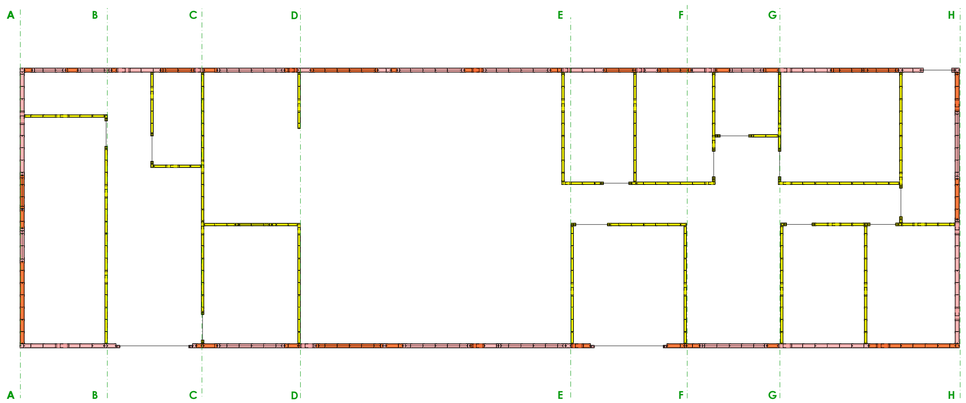

Data | REV. | Descrição | Responsável

Projeto Estrutural Light Steel Framing

AMAGGI

Informações do Projeto:
AMAGGI EXPORTAÇÃO E IMPORTAÇÃO LTDA.
RODOVIA BR 364, LOTE 06-A-1 KM 543,7,
GLEBA 25 ALTO PARAÍSO - RO

Descrição da Folha:
Cortes de painéis - PV1

Responsabilidade Técnica::
Engº Roberto Hiroyuki Nakamura
CREA PR-90790/D
ART.:
www.upriseframing.com.br
(42) 98813 - 7718

Up Rise

Link temporário para acesso do formulário DIGITAL.

Escala indicada

Revisão:
R0

Prancha
03

Detalhamento de Montagem

mm

IMPRIMIR COLORIDO E EM FOLHA A1

Emitido por cliente

As informações contidas neste desenho são exclusividades da Up rise framing.
não podem ser copiadas, reproduzidas sem autorização prévia.